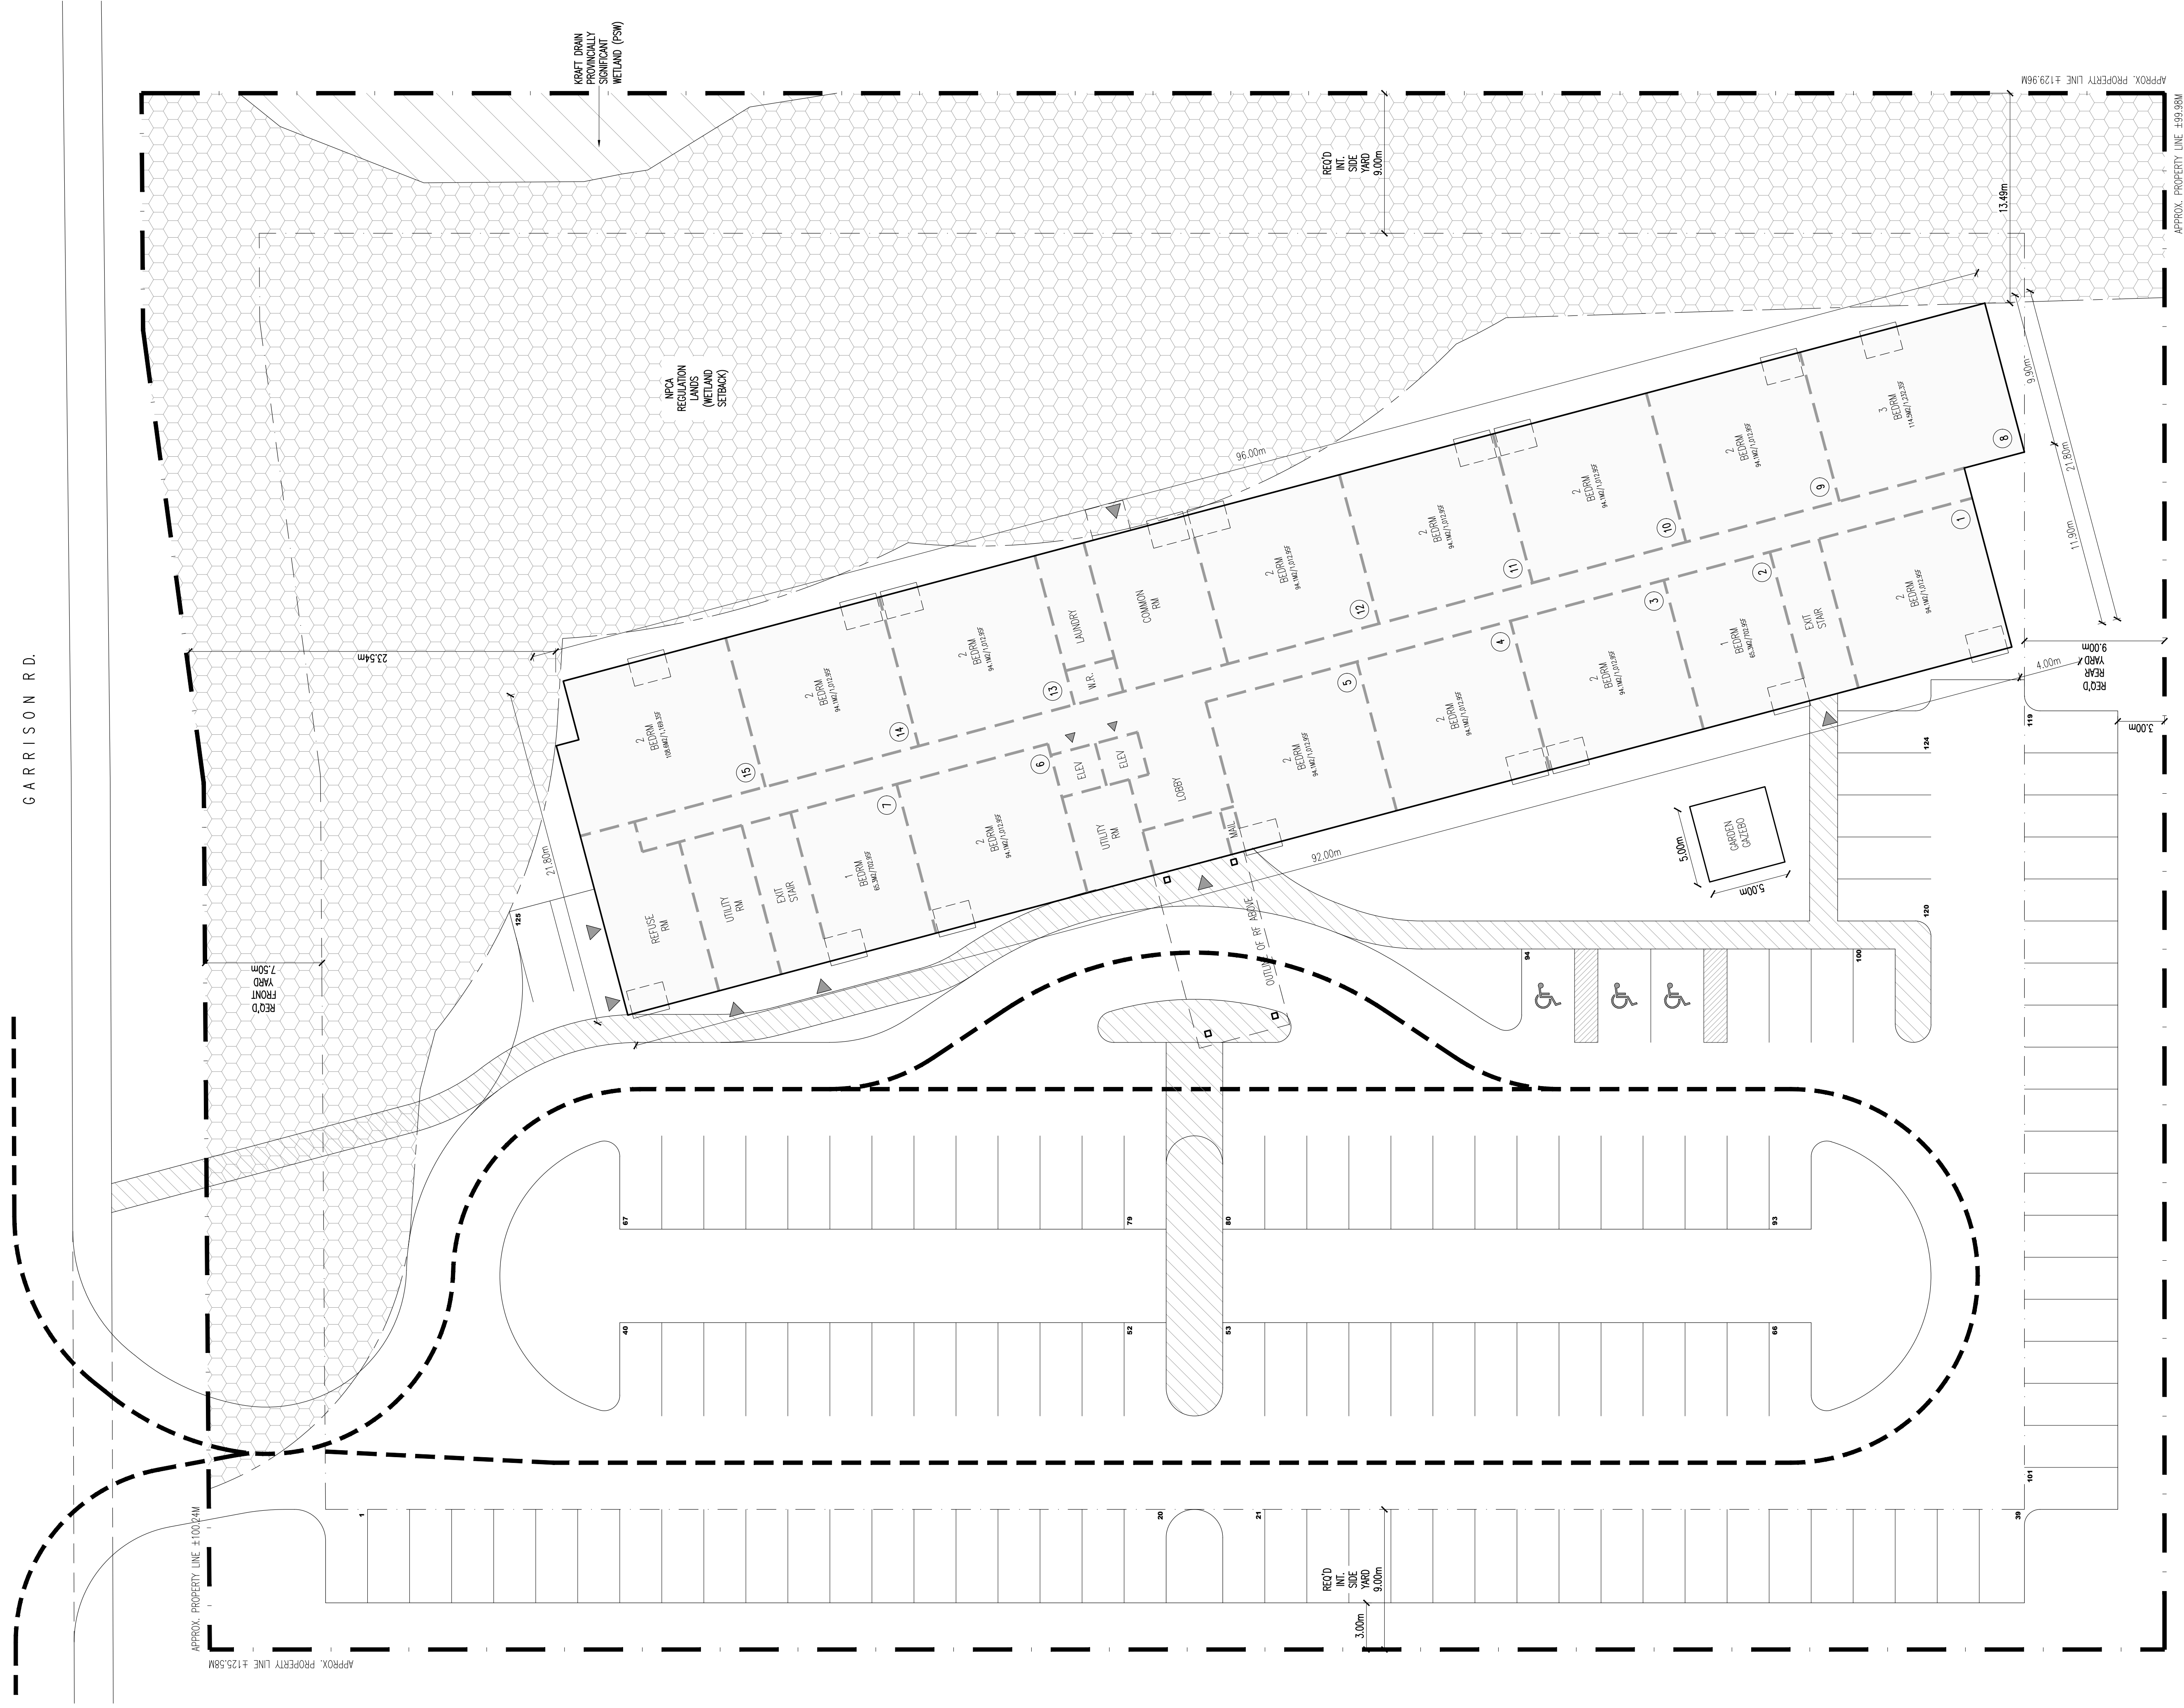


PROPOSED DWELLINGS	PARKING SPACES
GRD. FLR 3 BEDRM: 1 UNITS 2 BEDRM: 12 UNITS 1 BEDRM: 2 UNITS TOTAL: 15 UNITS	REQ'D: 125 (1.25 PER DWELLING) PROP'D: 125
TOTAL PROP'D UNITS: 85+15 = 100 UNITS	



PROPOSED SITE PLAN
SCALE: 1:200

job number:	revision number:
24-40	
drawing number:	

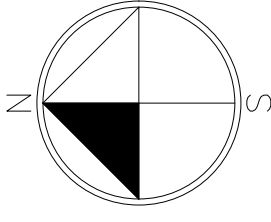
151

project title: PLAN STUDY
PROPOSED RESIDENTIAL BUILDING
825 GARRISON RD
FORT ERIE, ON

growing title: **DRAFT**
SITE PLAN STUDY

drawn by: TV	design by: LJM	plot scale: 1:1
approved by: MRM	scale: AS NOTED	
date: MARCH 28, 2025		

2M architects inc.
115 Lake Street
St. Catharines, ON
Canada L2R 5X7
Tel: 905-687-9777
Fax: 905-687-9997
2Marchitects@cogeco.net
www.2marchitects.ca

[illegible]

THESE DOCUMENTS ARE NOT TO BE SCALED.

THE DESIGN AND DOCUMENTS REMAIN THE PROPERTY OF THE ARCHITECT AND ARE PROTECTED BY LAW. THEY MAY NOT BE ALTERED WITHOUT THEIR EXPRESSED WRITTEN CONSENT. ALL DOCUMENTS ARE TO BE RETURNED AT COMPLETION OF WORK.

CONTRACTOR TO SITE VERIFY ALL DETAILS AND DIMENSIONS AND REPORT ANY AND ALL DISCREPANCIES TO THE ARCHITECT BEFORE COMMENCING WITH THAT RELATED PORTION OF THE WORK.

ONLY SIGNED SEALED AND STAMPED DOCUMENTS ARE TO BE USED FOR CONSTRUCTION PURPOSES.



revision number:	job number: 24-40
drawing number:	

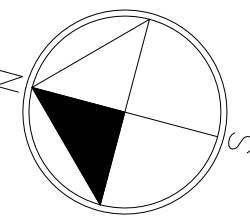
A1

project title: PLAN STUDY
PROPOSED RESIDENTIAL BUILDING

drawing title: **DRAFT**
PROPOSED GROUND FLOOR &
TYPICAL FLOOR

drawn by: TV		plot score: 1:1	
design by: LJM		scale: AS NOTED	
approved by: MRM		date: MARCH 28, 2025	

2M architects inc.
115 Lake Street
St. Catharines, ON
Canada L2R 5X7
Tel: 905-687-9777
Fax: 905-687-9997
2Marchitects@cogeco.net
www.2marchitects.ca

[illegible]

THESE DOCUMENTS ARE NOT TO BE SCALED.

THE DESIGN AND DIMENSIONS REMAIN THE PROPERTY OF THE ARCHITECT AND BE PROVIDED BY THE ARCHITECT. THE CONTRACTOR SHALL NOT ALTER OR MODIFY ANY OF THE INFORMATION HEREON WITHOUT THE WRITTEN CONSENT. ALL DOCUMENTS TO BE RETURNED AT COMPLETION OF WORK.

CONTRACTOR TO SITE VERIFY ALL DETAILS AND DIMENSIONS AND REPORT ANY AND ALL DISCREPANCIES TO THE ARCHITECT BEFORE COMMENCING WITH THAT RELATED PORTION OF THE WORK.

ONLY SIGNED, SEALED AND STAMPED DOCUMENTS ARE TO BE USED FOR CONSTRUCTION PURPOSES.

